


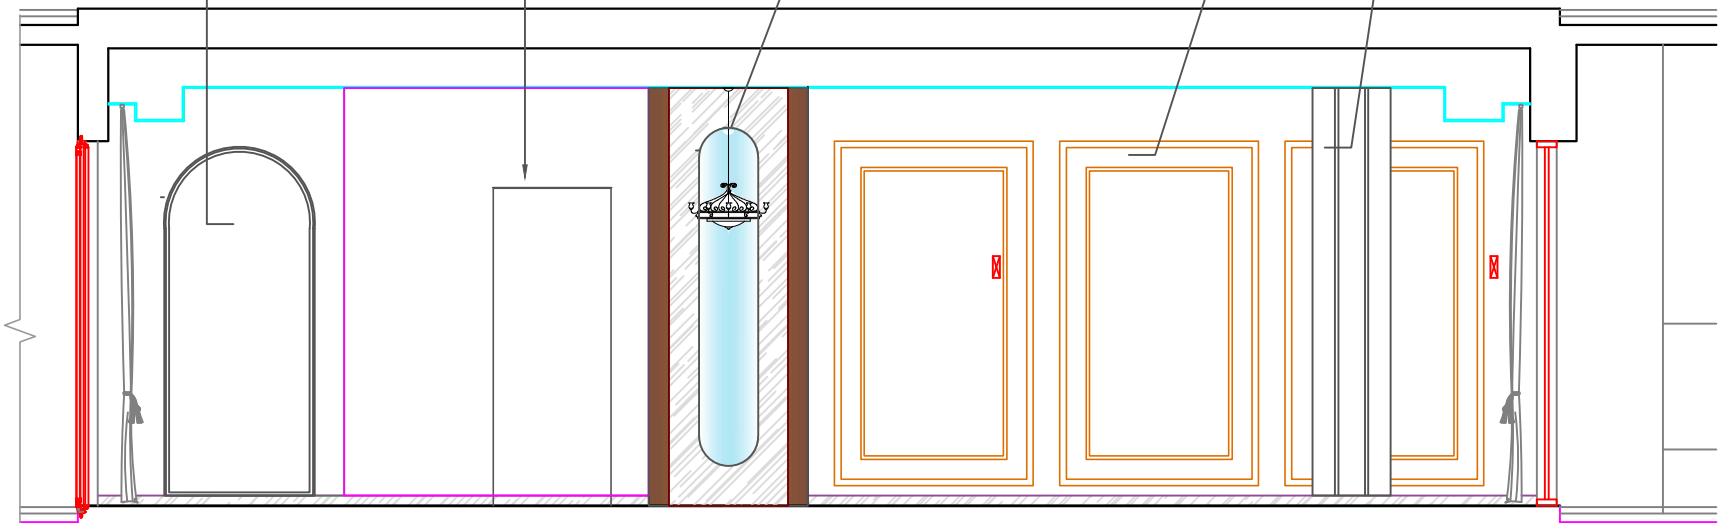
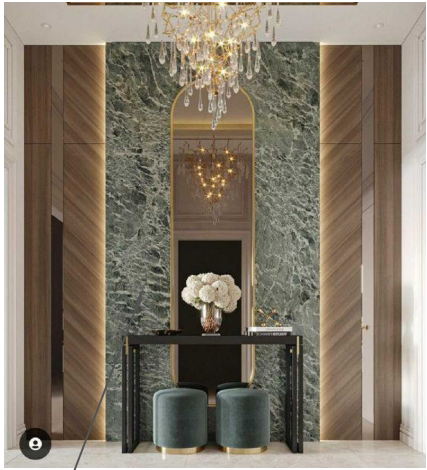
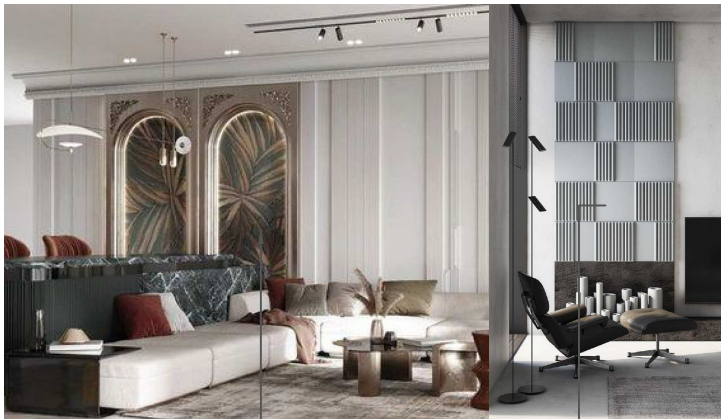


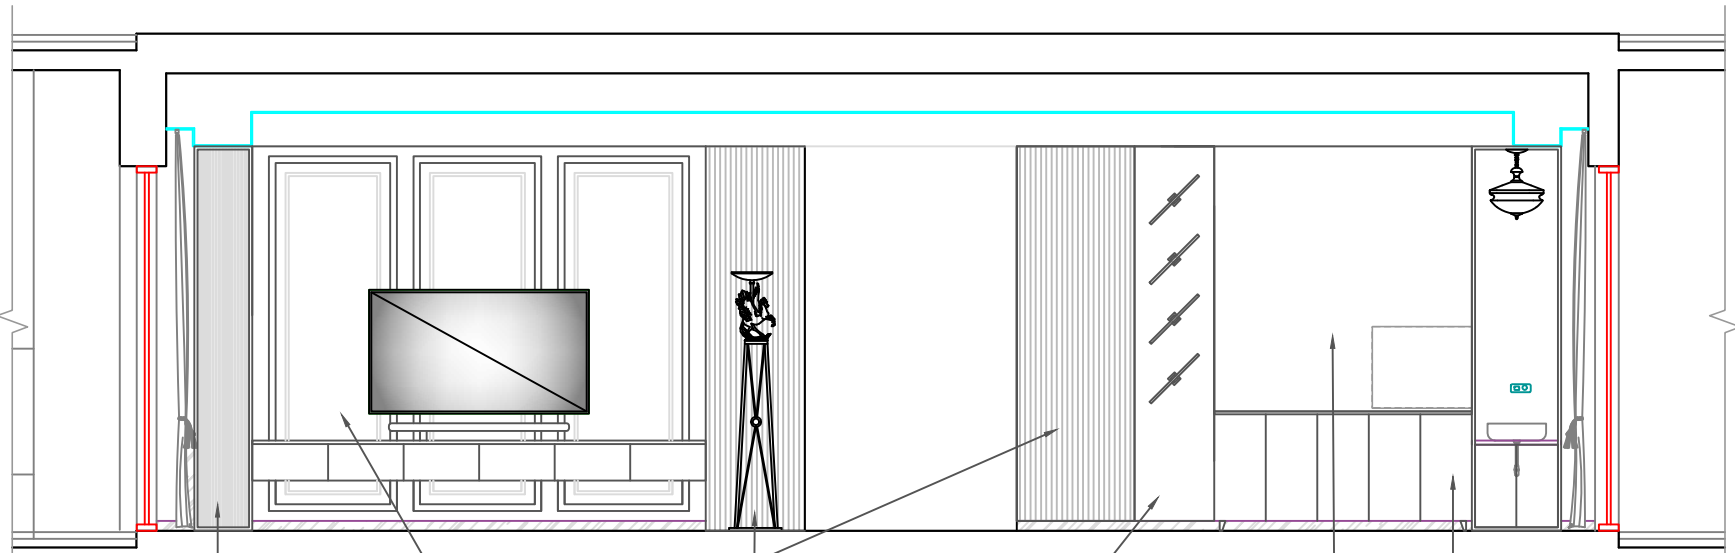

SECTION B-B'

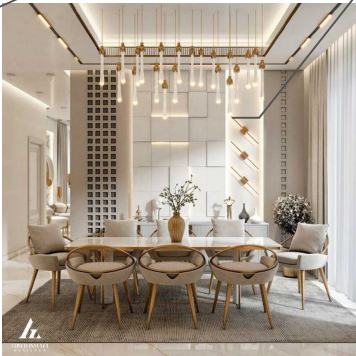

SECTION D-D'

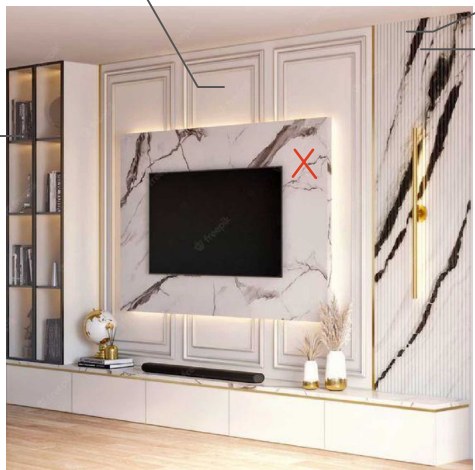

TITLE

Construction and Demolition Layout

GENERAL NOTES

ALL THE DIMENSIONS INDICATED ARE IN INCHES AND ARE FINISHED DIMENSIONS ALL THE DIMENSIONS INDICATED IN THIS DRAWING ARE TO BE CHECKED AND VARIFIED AT SITE PRIOR TO THE COMMENCEMENT OF WORK BY THE CONTRACTOR

BRANCH OFFICE:

B-70 DEWAN CENTER,
S.V. ROAD,NR. JOG. RLY.
STATION, JOGESHWARI (WEST)
MUMBAI 4000102
MOB : +91 9821006024
: + 91 9819045847

CLIENT

PROPOSED INTERIOR
LAYOUT FOR
RESIDENIAL AT
Avyaan Piramal .

DWG. NO.	01
DRAWN BY	AFSHEEN
CHECKED BY	SHOEB
SCALE	NTS
DATE	24-05-24

NORTH

ALL MEASUREMENT MUST
BE CHECKED

WEBSITE:

arctisticdesign.com

EMAIL

info@arctisticdesign.com

THIS DRAWING IS
COPYRIGHTED. IT IS
PROPERTY OF ARCTISTIC
DESIGN & ASSOCIATE AND IS
NOT TO BE REPRODUCED,
SUPPLIED,HANDED OVER TO
A THIRD PARTY OR USED
FOR PURPOSE OTHER THEN
FOR WHICH IT HAS BEEN
INTENDED.